
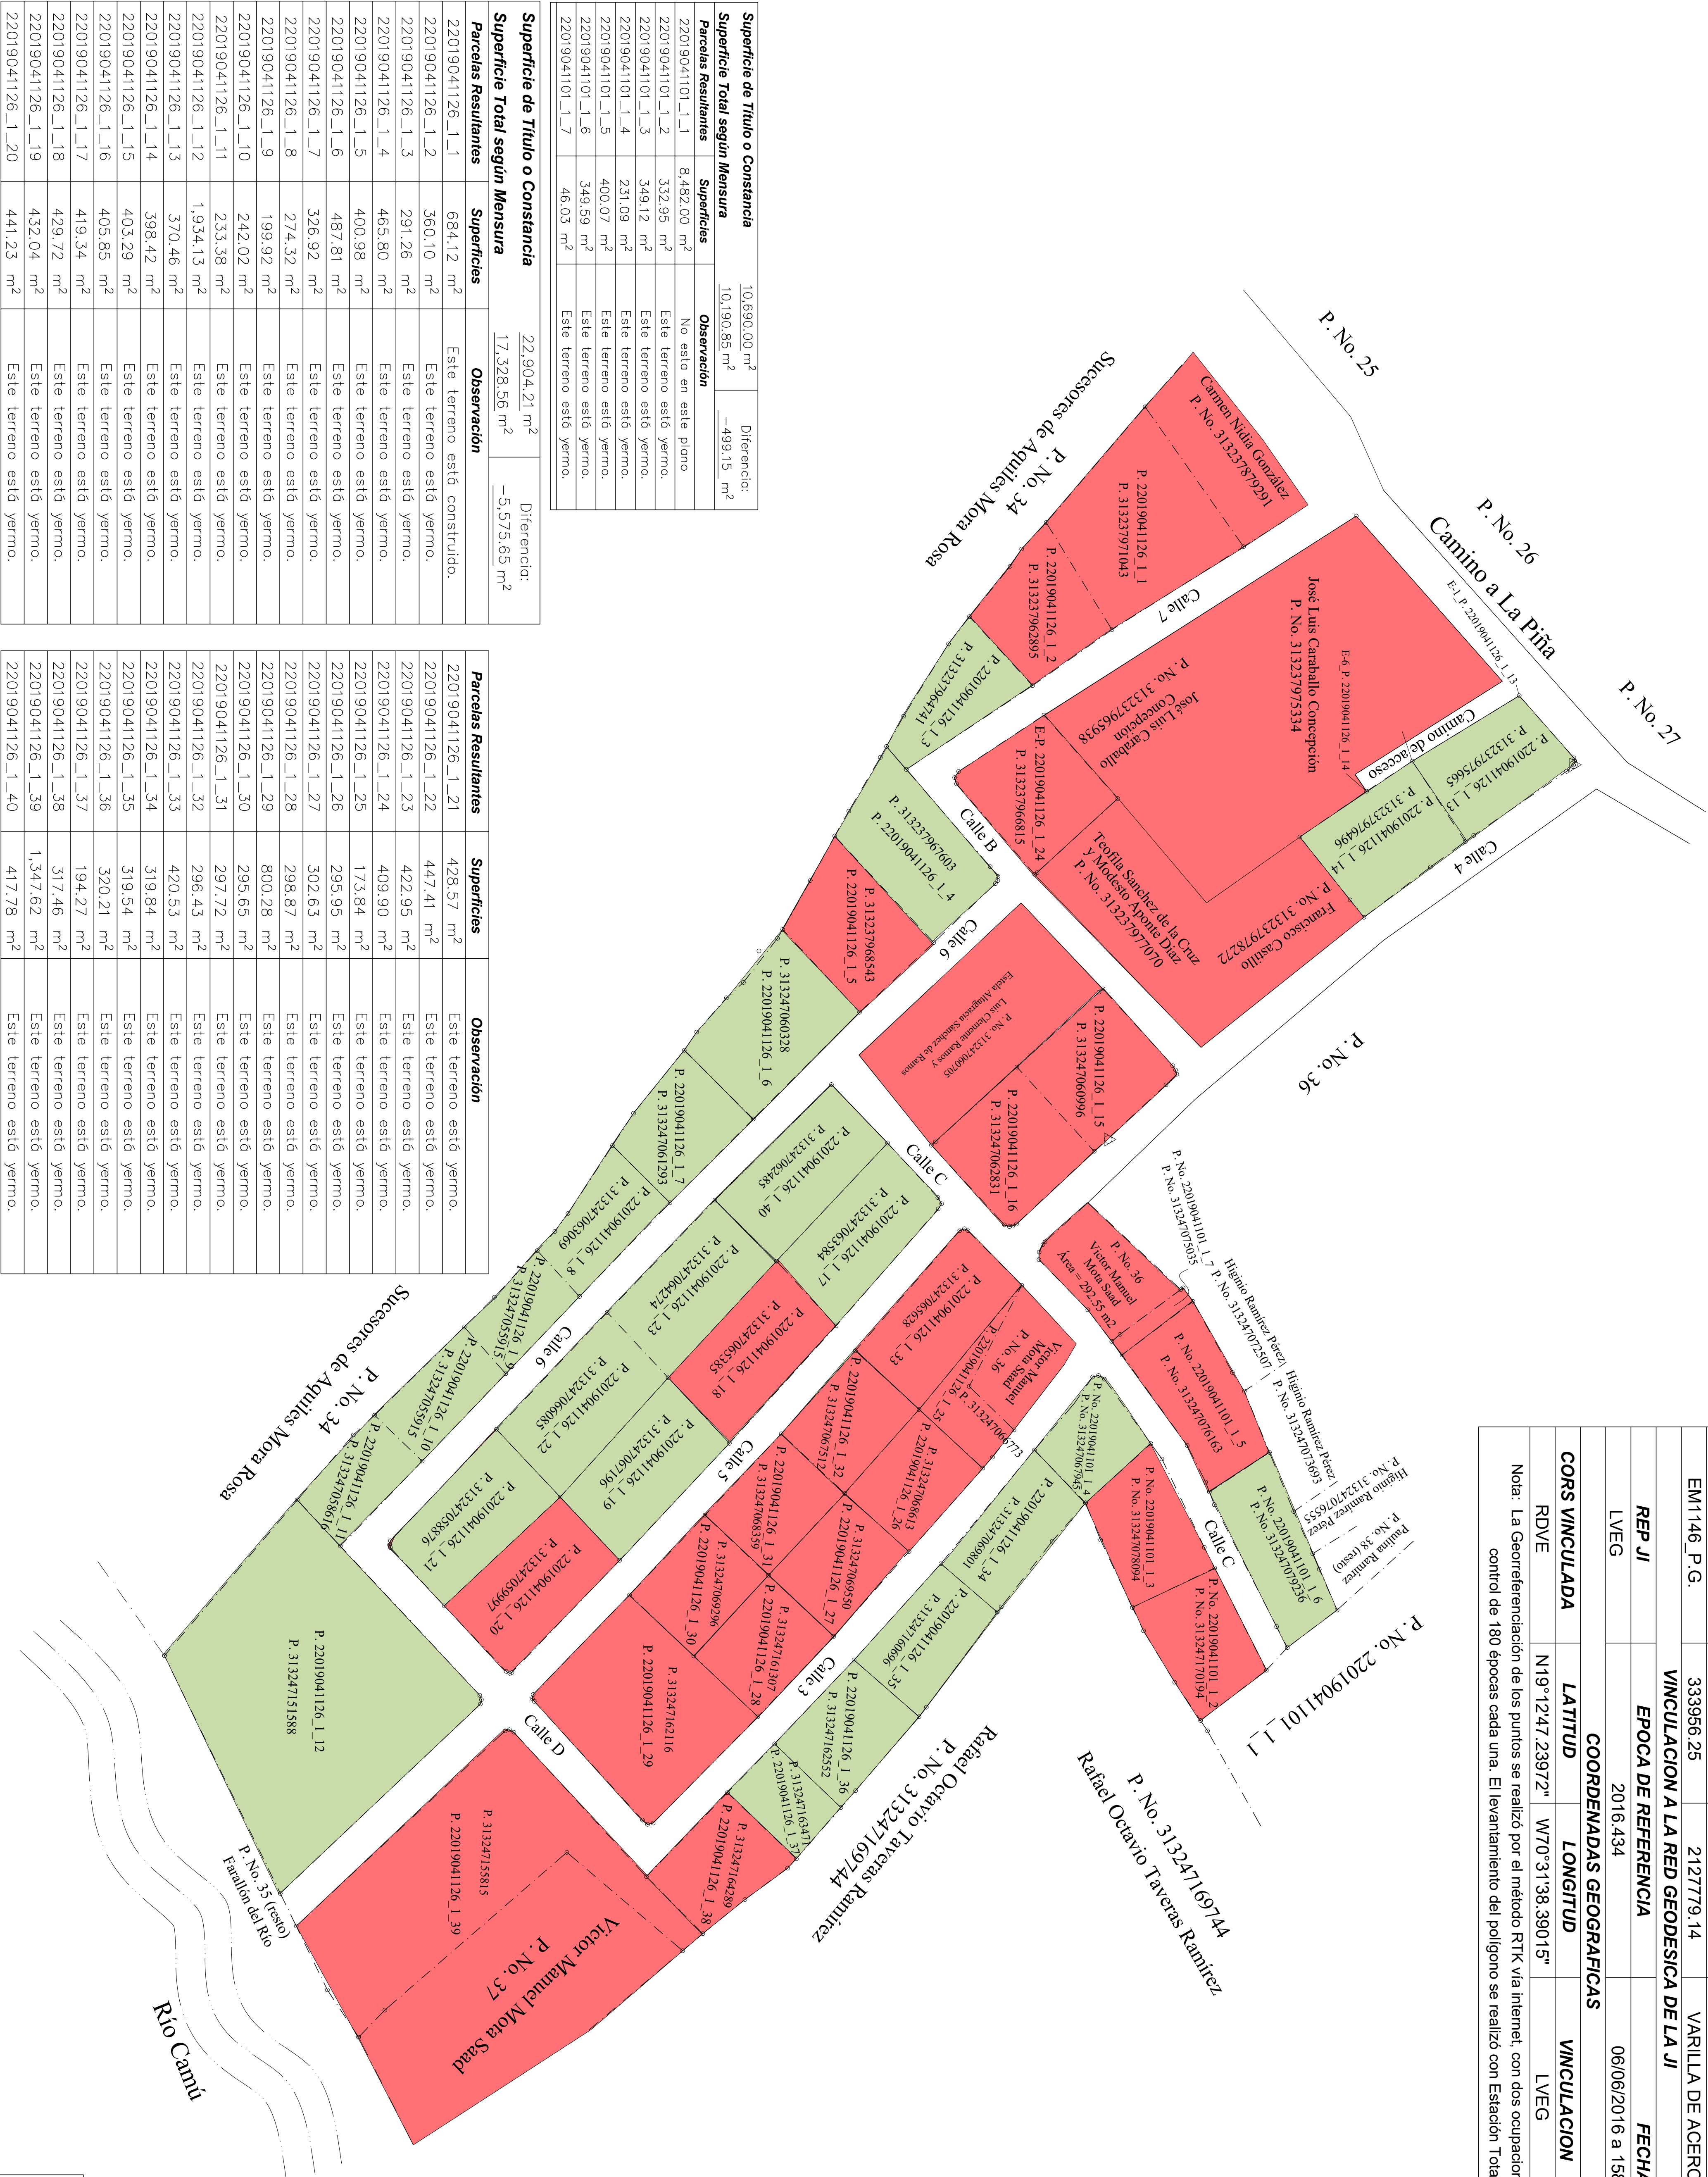


PUNTOS GEORREFERENCIADOS (COORDENADAS UTM ZONA 19N)				
FACTOR DE ESCALA COMBINADO: 0.9999207052				
PUNTO	X	Y	MATERIALIZACION	FECHA
EM1145_P.G.	334021.72	2127697.79	VARILLA DE ACERO	25/04/2019
EM1146_P.G.	333956.25	212779.14	VARILLA DE ACERO	25/04/2019
VINCULACION A LA RED GEODESICA DE LA JI				
REP JI	EPOCA DE REFERENCIA		FECHA	
LVEG	2016.434		06/06/2016 a 158 D. J. 2016	
COORDENADAS GEOGRAFICAS				
CORS VINCULADA	LATTITUD	LONGITUD	VINCULACION	FECHA
RDVE	N19°12'47.23972"	W70°31'38.39015"	LVEG	25/05/2017
Nota: La Georreferenciación de los puntos se realizó por el método RTK vía internet, con dos ocupaciones en calidad control de 180 épocas cada una. El levantamiento del polígono se realizó con Estación Total.				

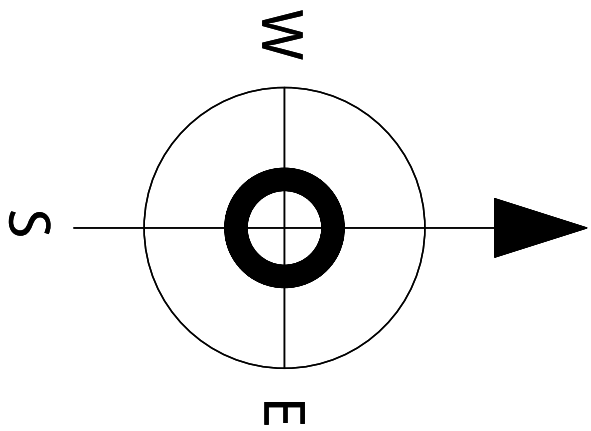

Superficie de Título o Constancia		10,690.00 m²	Diferencia: -499.15 m²
Superficie Total según Mensura		10,190.85 m²	
Parcelas Resultantes	Superficies	Observación	
22019041101_1.1	8,482.00 m²	No está en este plano	
22019041101_1.2	332.95 m²	Este terreno está yermo.	
22019041101_1.3	349.12 m²	Este terreno está yermo.	
22019041101_1.4	231.09 m²	Este terreno está yermo.	
22019041101_1.5	400.07 m²	Este terreno está yermo.	
22019041101_1.6	349.59 m²	Este terreno está yermo.	
22019041101_1.7	46.03 m²	Este terreno está yermo.	

Superficie de Título o Constancia		22,904.21 m²	Diferencia: -5,575.65 m²
Superficie Total según Mensura		17,328.56 m²	
Parcelas Resultantes	Superficies	Observación	
22019041126_1.1	684.12 m²	Este terreno está construido.	
22019041126_1.2	360.10 m²	Este terreno está yermo.	
22019041126_1.3	291.26 m²	Este terreno está yermo.	
22019041126_1.4	465.80 m²	Este terreno está yermo.	
22019041126_1.5	400.98 m²	Este terreno está yermo.	
22019041126_1.6	487.81 m²	Este terreno está yermo.	
22019041126_1.7	326.92 m²	Este terreno está yermo.	
22019041126_1.8	274.32 m²	Este terreno está yermo.	
22019041126_1.9	199.92 m²	Este terreno está yermo.	
22019041126_1.10	242.02 m²	Este terreno está yermo.	
22019041126_1.11	233.38 m²	Este terreno está yermo.	
22019041126_1.12	1,934.13 m²	Este terreno está yermo.	
22019041126_1.13	370.46 m²	Este terreno está yermo.	
22019041126_1.14	398.42 m²	Este terreno está yermo.	
22019041126_1.15	403.29 m²	Este terreno está yermo.	
22019041126_1.16	405.85 m²	Este terreno está yermo.	
22019041126_1.17	419.34 m²	Este terreno está yermo.	
22019041126_1.18	429.72 m²	Este terreno está yermo.	
22019041126_1.19	432.04 m²	Este terreno está yermo.	
22019041126_1.20	441.23 m²	Este terreno está yermo.	

Parcelas Resultantes	Superficies	Observación
22019041126_1.21	428.57 m²	Este terreno está yermo.
22019041126_1.22	447.41 m²	Este terreno está yermo.
22019041126_1.23	422.95 m²	Este terreno está yermo.
22019041126_1.24	409.90 m²	Este terreno está yermo.
22019041126_1.25	173.84 m²	Este terreno está yermo.
22019041126_1.26	295.95 m²	Este terreno está yermo.
22019041126_1.27	302.63 m²	Este terreno está yermo.
22019041126_1.28	298.87 m²	Este terreno está yermo.
22019041126_1.29	800.28 m²	Este terreno está yermo.
22019041126_1.30	295.65 m²	Este terreno está yermo.
22019041126_1.31	297.72 m²	Este terreno está yermo.
22019041126_1.32	296.43 m²	Este terreno está yermo.
22019041126_1.33	420.53 m²	Este terreno está yermo.
22019041126_1.34	319.84 m²	Este terreno está yermo.
22019041126_1.35	319.54 m²	Este terreno está yermo.
22019041126_1.36	320.21 m²	Este terreno está yermo.
22019041126_1.37	194.27 m²	Este terreno está yermo.
22019041126_1.38	317.46 m²	Este terreno está yermo.
22019041126_1.39	1,347.62 m²	Este terreno está yermo.
22019041126_1.40	417.78 m²	Este terreno está yermo.



REPÚBLICA DOMINICANA

PODER JUDICIAL

JURISDICCIÓN INDOCTRINARIA

DIRECCIÓN REGIONAL DE REGISTRO Y CATASTROS

PLANO GENERAL

OPERACIÓN: DESLINDE

DESIGNACIÓN CATASTRAL DE ORIGEN No. (G)P/ No. 35 PRE D.C. No. 32

DESIGNACIÓN TEMPORAL No. (G)P/ No. 2019041126_1.1 (a) 2019041126_1.40

PROVINCIA: LA VEGA

MUNICIPIO: CONCEPCION DE LA VEGA

SECCION: SAVANAHES

LUGAR: LUGAR FRANCISCO MORA

REFERENCIAS DE UBICACION: EN LA INTERSECCION FORMADA POR EL CAMINO A LA PIA CON LA CALLE 4 Y CALLE 7 EN LA LITORAL DEL MUNICIPIO DE CONCEPCION DE LA VEGA.

SUPERFICIE PARCELA: CODIA 4080

ESCALA: 1:150

HECHO EN: LA VEGA

FECHA: 25/05/2017

DESIGNACION CATASTRAL POSICIONAL:

ELADIO R. MARTE

AGREMENSOR

CODIA 4080

La Vega

FECHA Y FIRMA DEL DIRECTOR

DIRECCION REGIONAL DE REGISTRO Y CATASTROS

LA VEGA